


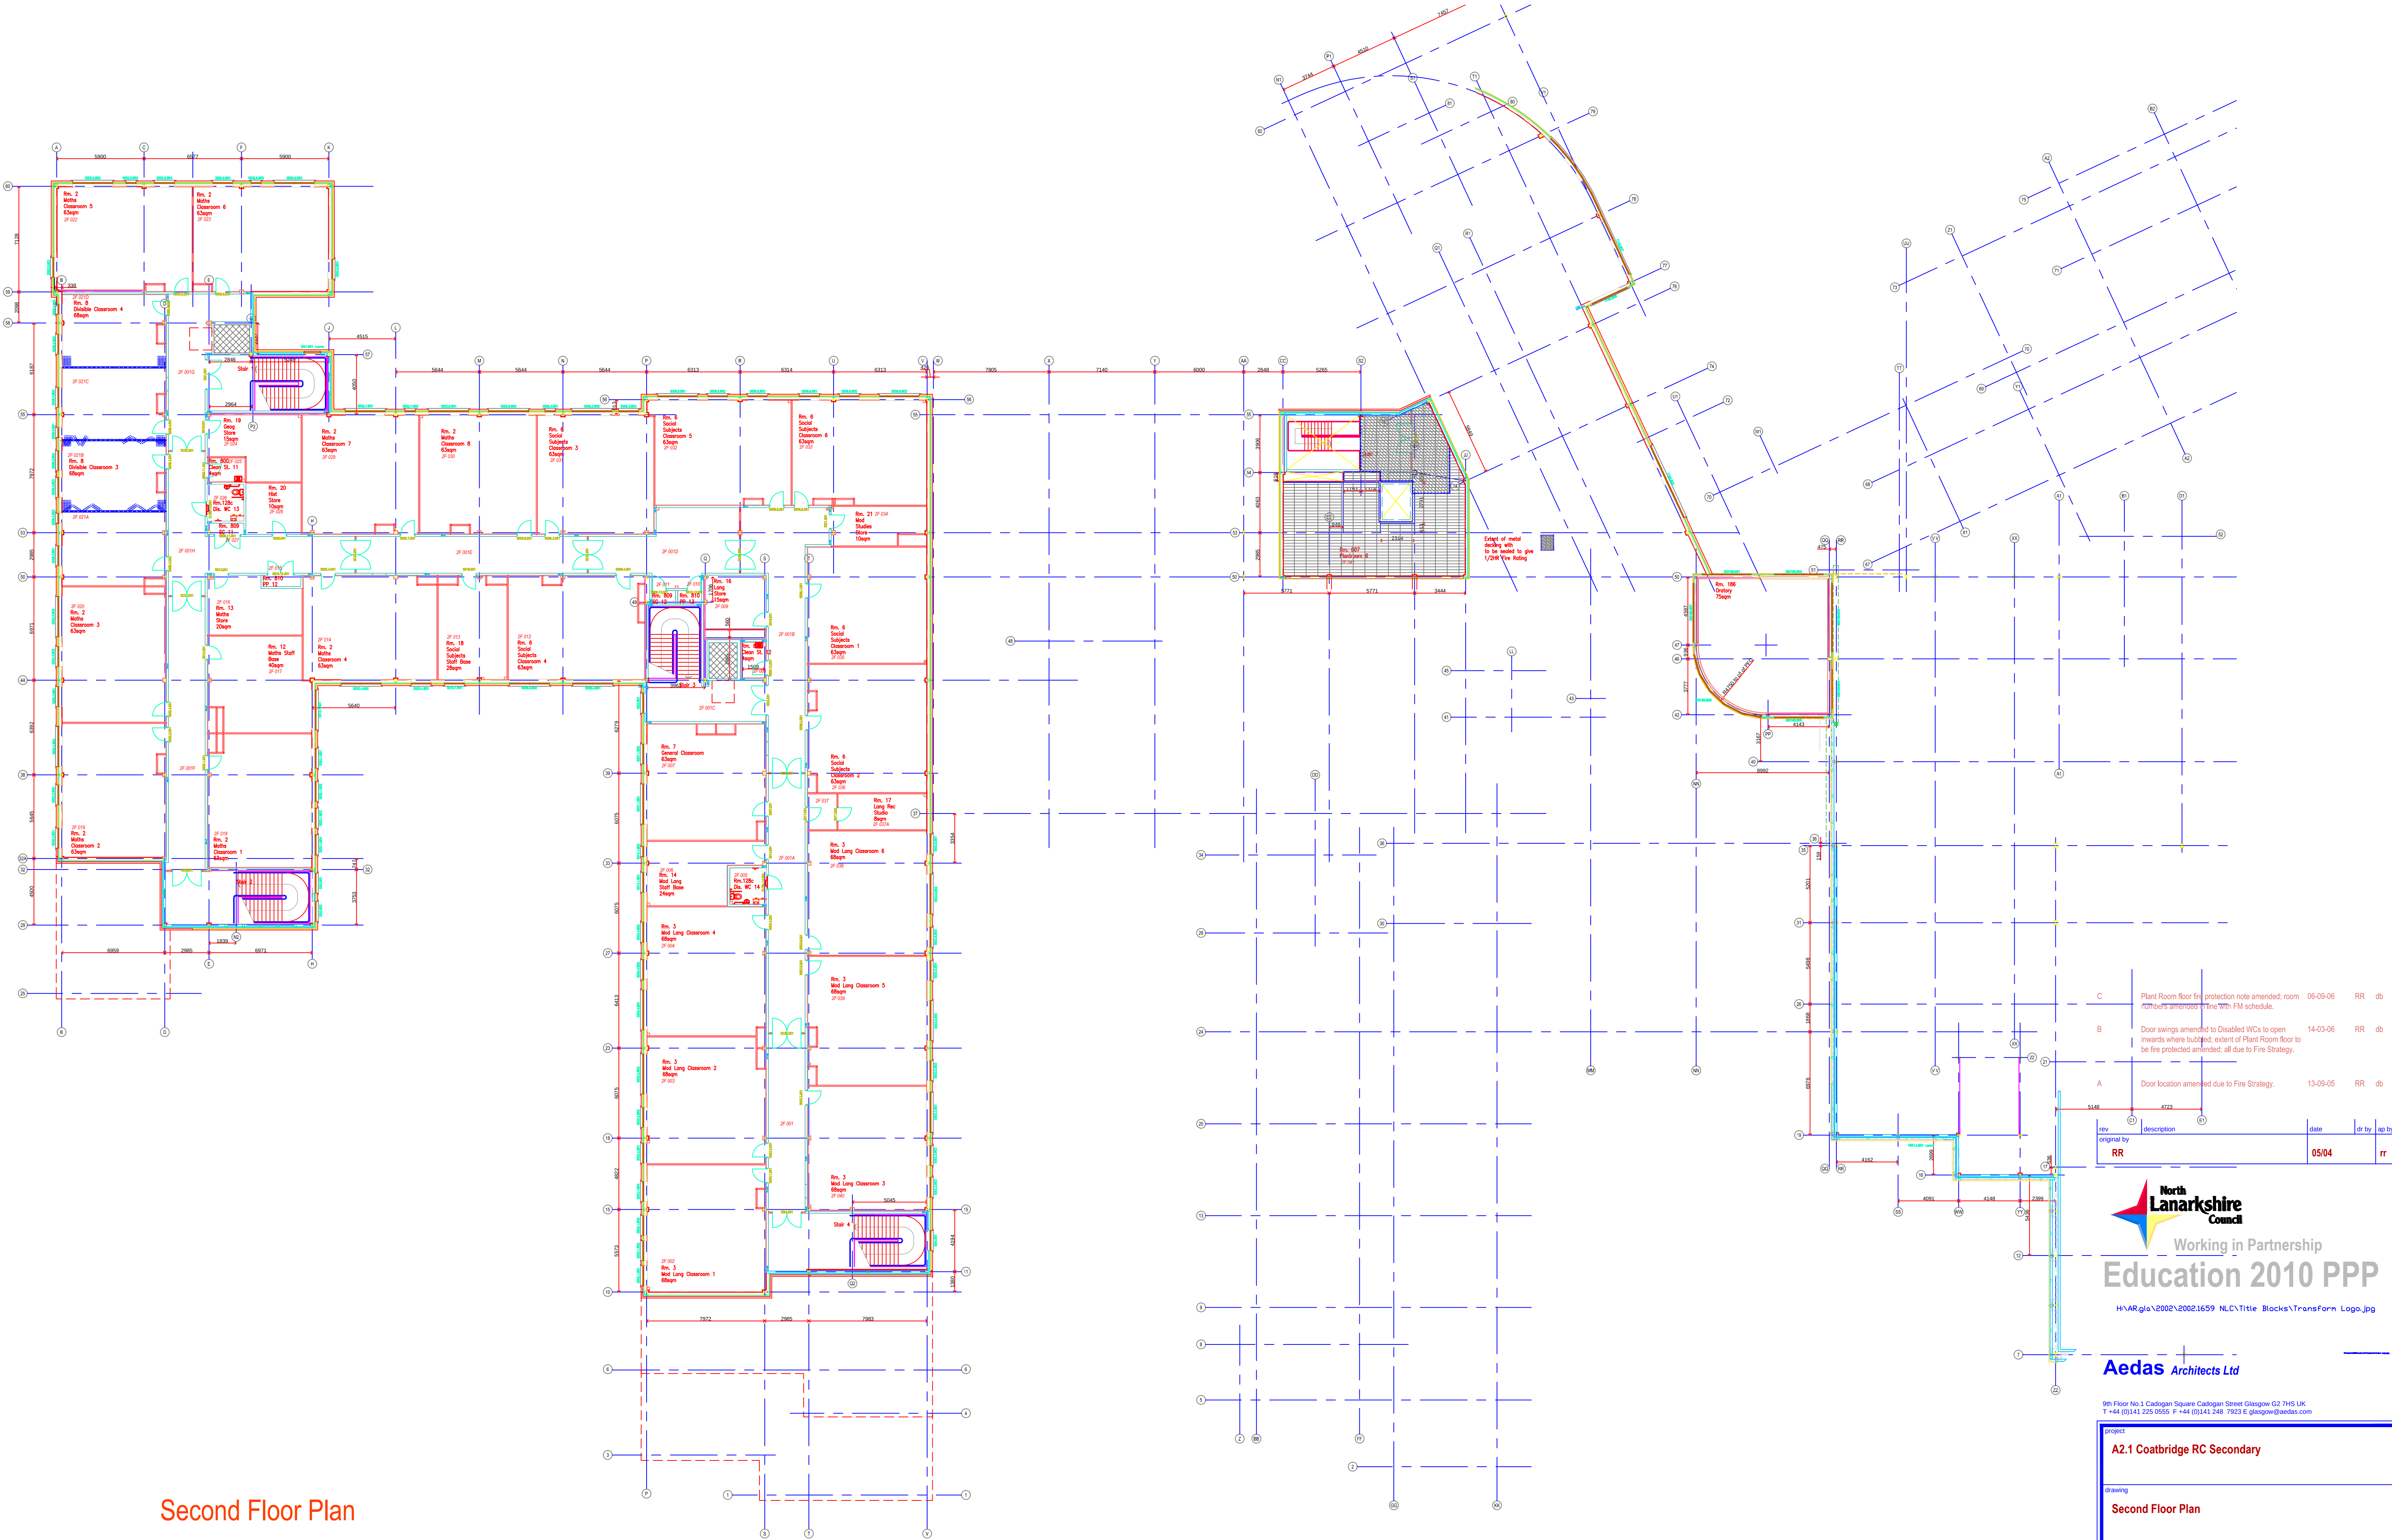

Second Floor Plan

C		Plant Room floor fire protection note amended; room numbers amended to line with FM schedule.	06-09-06	RR	db
B		Door swings amended to Disabled WC's to open inwards where bubbled; extent of Plant Room floor to be fire protected amended; all due to Fire Strategy.	14-03-06	RR	db
A		Door location amended due to Fire Strategy.	13-09-05	RR	db
rev	description		date	dr	ap
original by	RR		05/04	rr	



Working in Partnership
Education 2010 PPP

H:\AR\glc\2002\20021659_NLC\Title Blocks\Transform Logo.jpg

Aedas Architects Ltd

9th Floor No. 1 Cadogan Square Cadogan Street Glasgow G2 7HS UK
T +44 (0)141 225 0555 F +44 (0)141 248 7923 E glasgow@aedas.com

Project		A2.1 Coatbridge RC Secondary	
Drawing		Second Floor Plan	
computer file	plot date		06-09-06
project number	scale		1:200 @ A1
2002.01659.001			
drawing number	rev	issue status	
A2.1_CA_L(00)2_003	C	CA	

This drawing is to be read in conjunction with all related drawings. Do not scale from this drawing. All dimensions must be checked and verified on site before commencing any work or producing shop drawings. The originator should be notified immediately of any discrepancy. This drawing is copyright and remains the property of Aedas Architects.